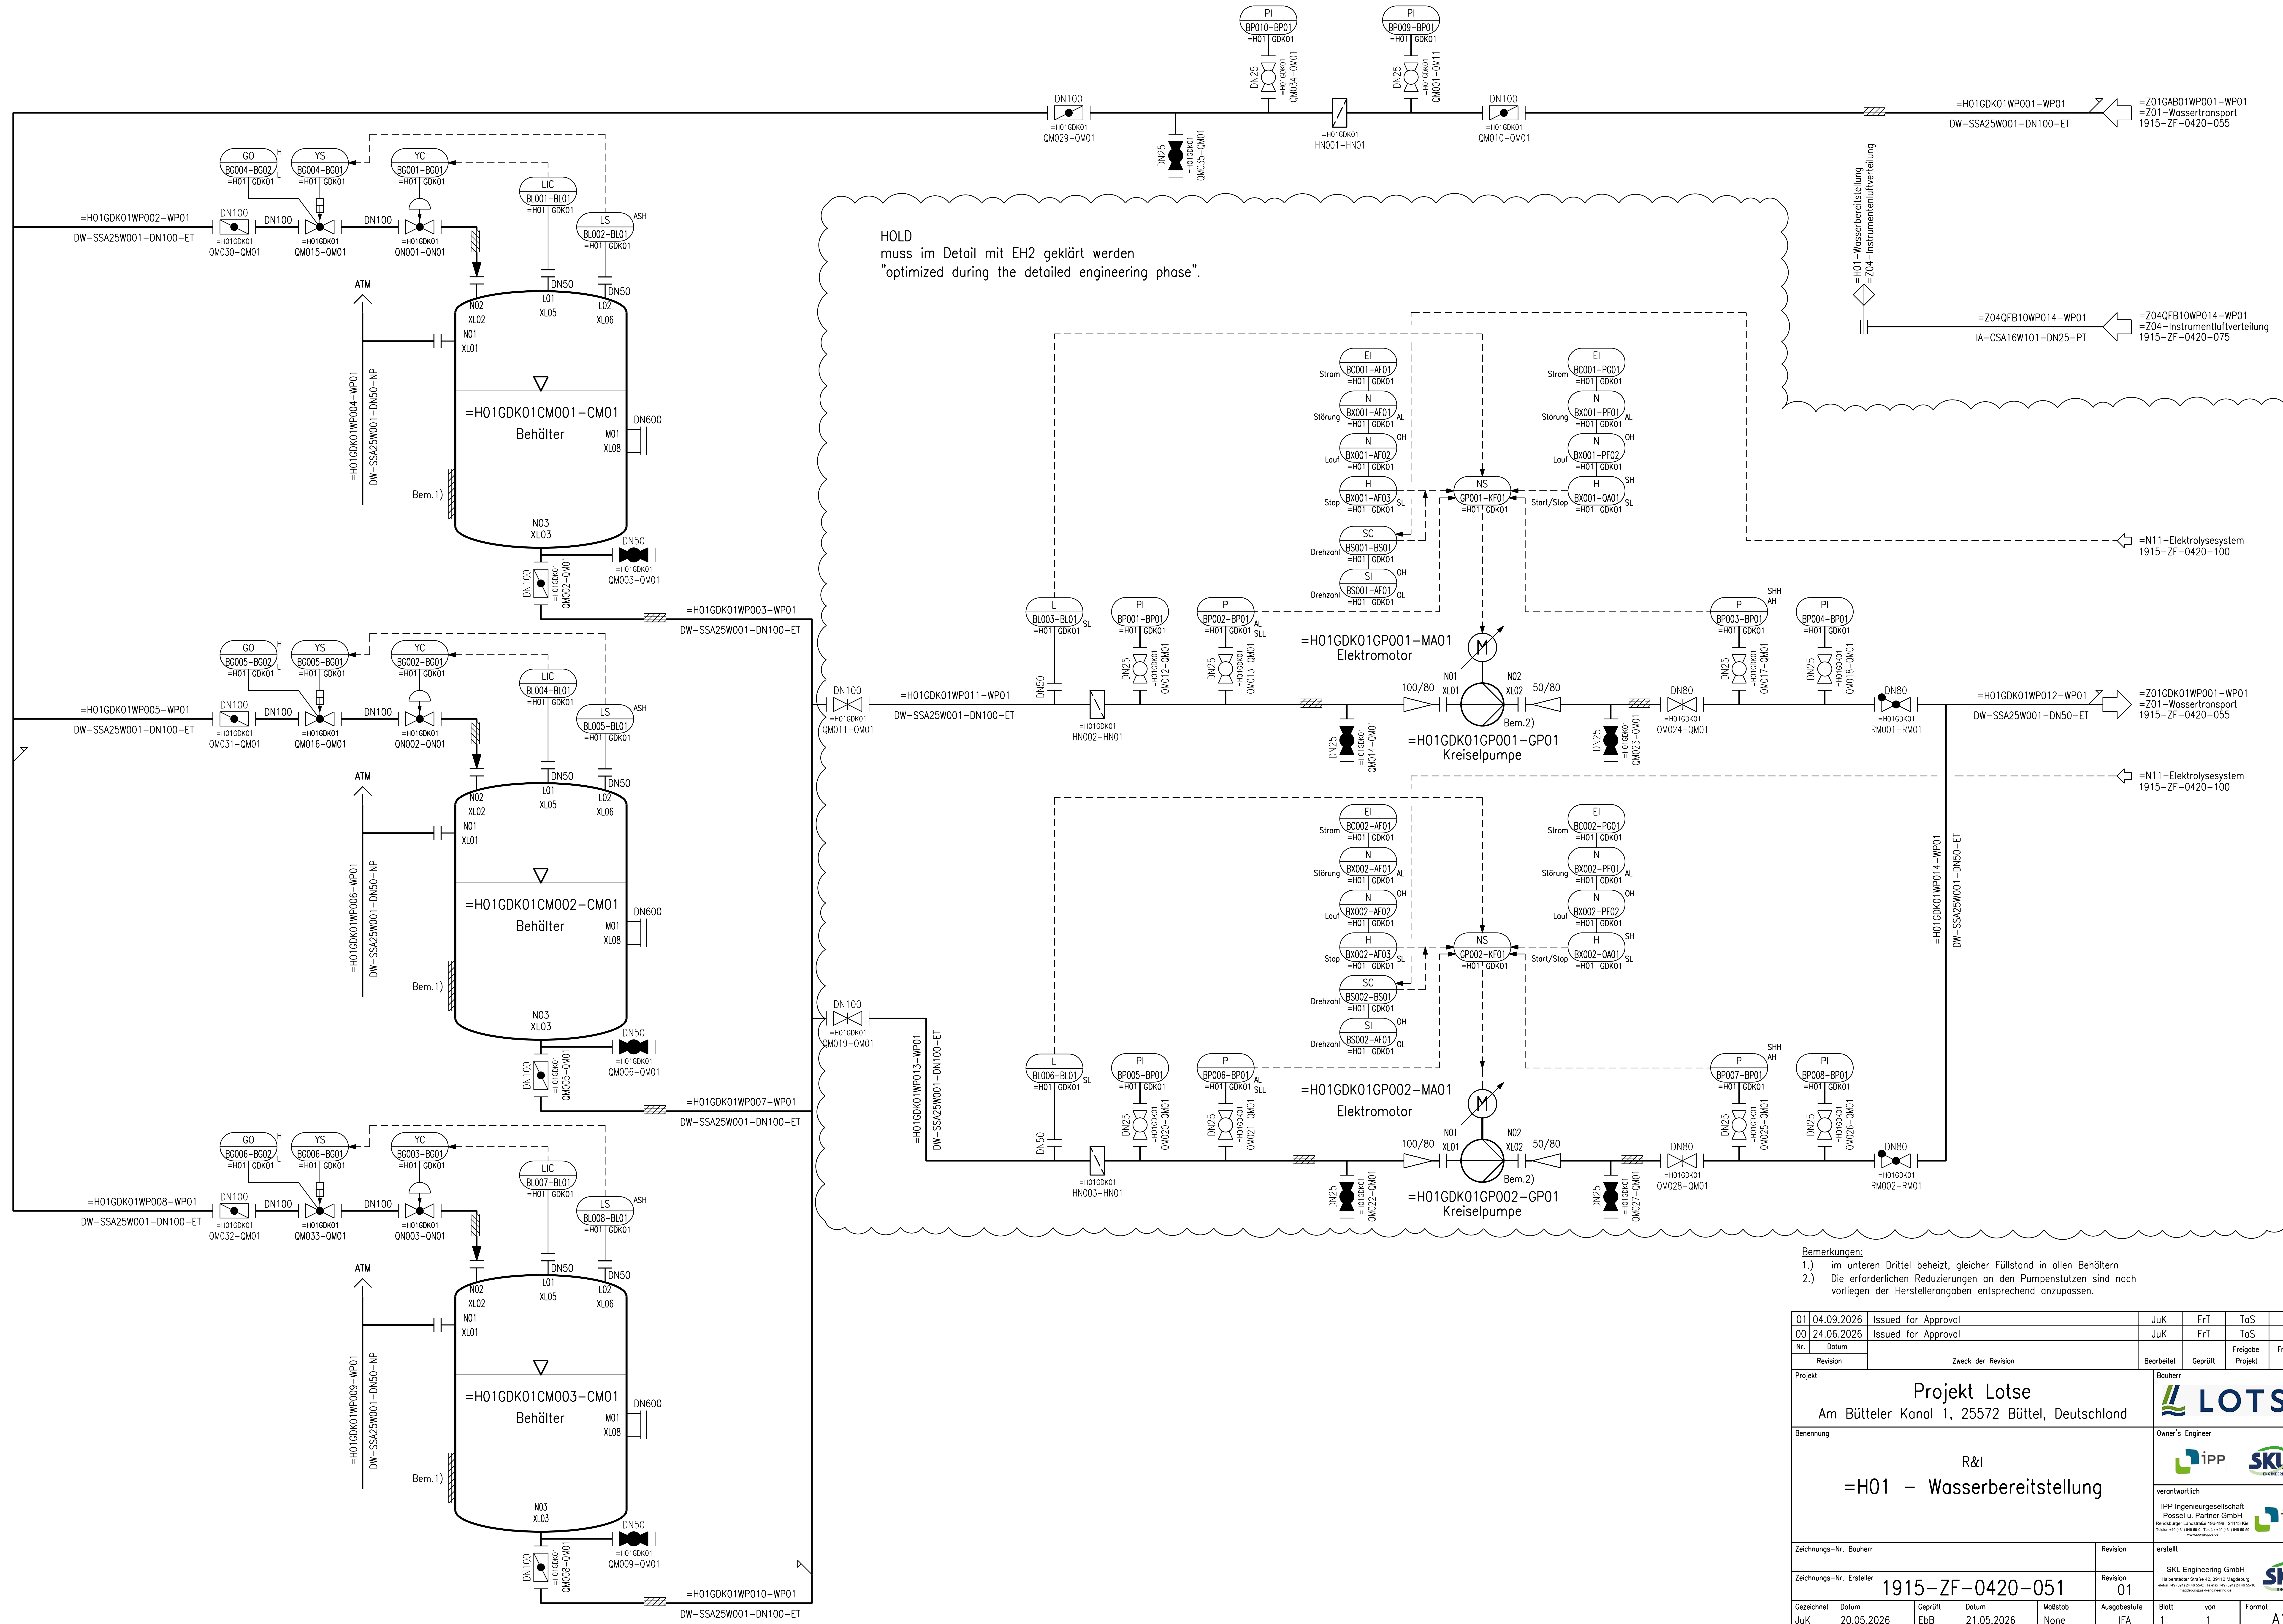

HOLD
muss im Detail mit EH2 geklärt werden
"optimized during the detailed engineering phase".

Bemerkungen:
1.) im unteren Drittel beheizt, gleicher Füllstand in allen Behältern
2.) Die erforderlichen Reduzierungen an den Pumpenstutzen sind nach vorliegen der Herstellerangaben entsprechend anzupassen.

Nr.	Datum	Zweck der Revision	Bearbeitet	Geprüft	Freigabe Projekt	Freigabe AG
01	04.09.2026	Issued for Approval	JuK	FrT	TaS	
00	24.06.2026	Issued for Approval	JuK	FrT	TaS	
Revision						

Projekt

Projekt Lotse

Am Bütteler Kanal 1, 25572 Büttel, Deutschland

Bauherr
LOTSE

Benennung

R&I

=H01 - Wasserbereitstellung

Owner's Engineer

verantwortlich
IPP Ingenieurgesellschaft
Possel u. Partner GmbH
Rendsburger Landstraße 196-198, 24113 Kiel
Telefon +49 (431) 649 59-0; Telefax +49 (431) 649 59-59
www.ipp-gruppe.de

Zeichnungs-Nr. Bauherr
Revision

Zeichnungs-Nr. Ersteller 1915-ZF-0420-051
Revision 01

erstellt
SKL Engineering GmbH
Halberstädter Straße 42, 39112 Magdeburg
Telefon +49 (391) 24 46 55-0; Telefax +49 (391) 24 46 55-10
magdeburg@skl-engineering.de

Gezeichnet	Datum	Geprüft	Datum	Maßstab	Ausgabestufe	Blatt	von	Format
JuK	20.05.2026	EbB	21.05.2026	None	IFA	1	1	A1