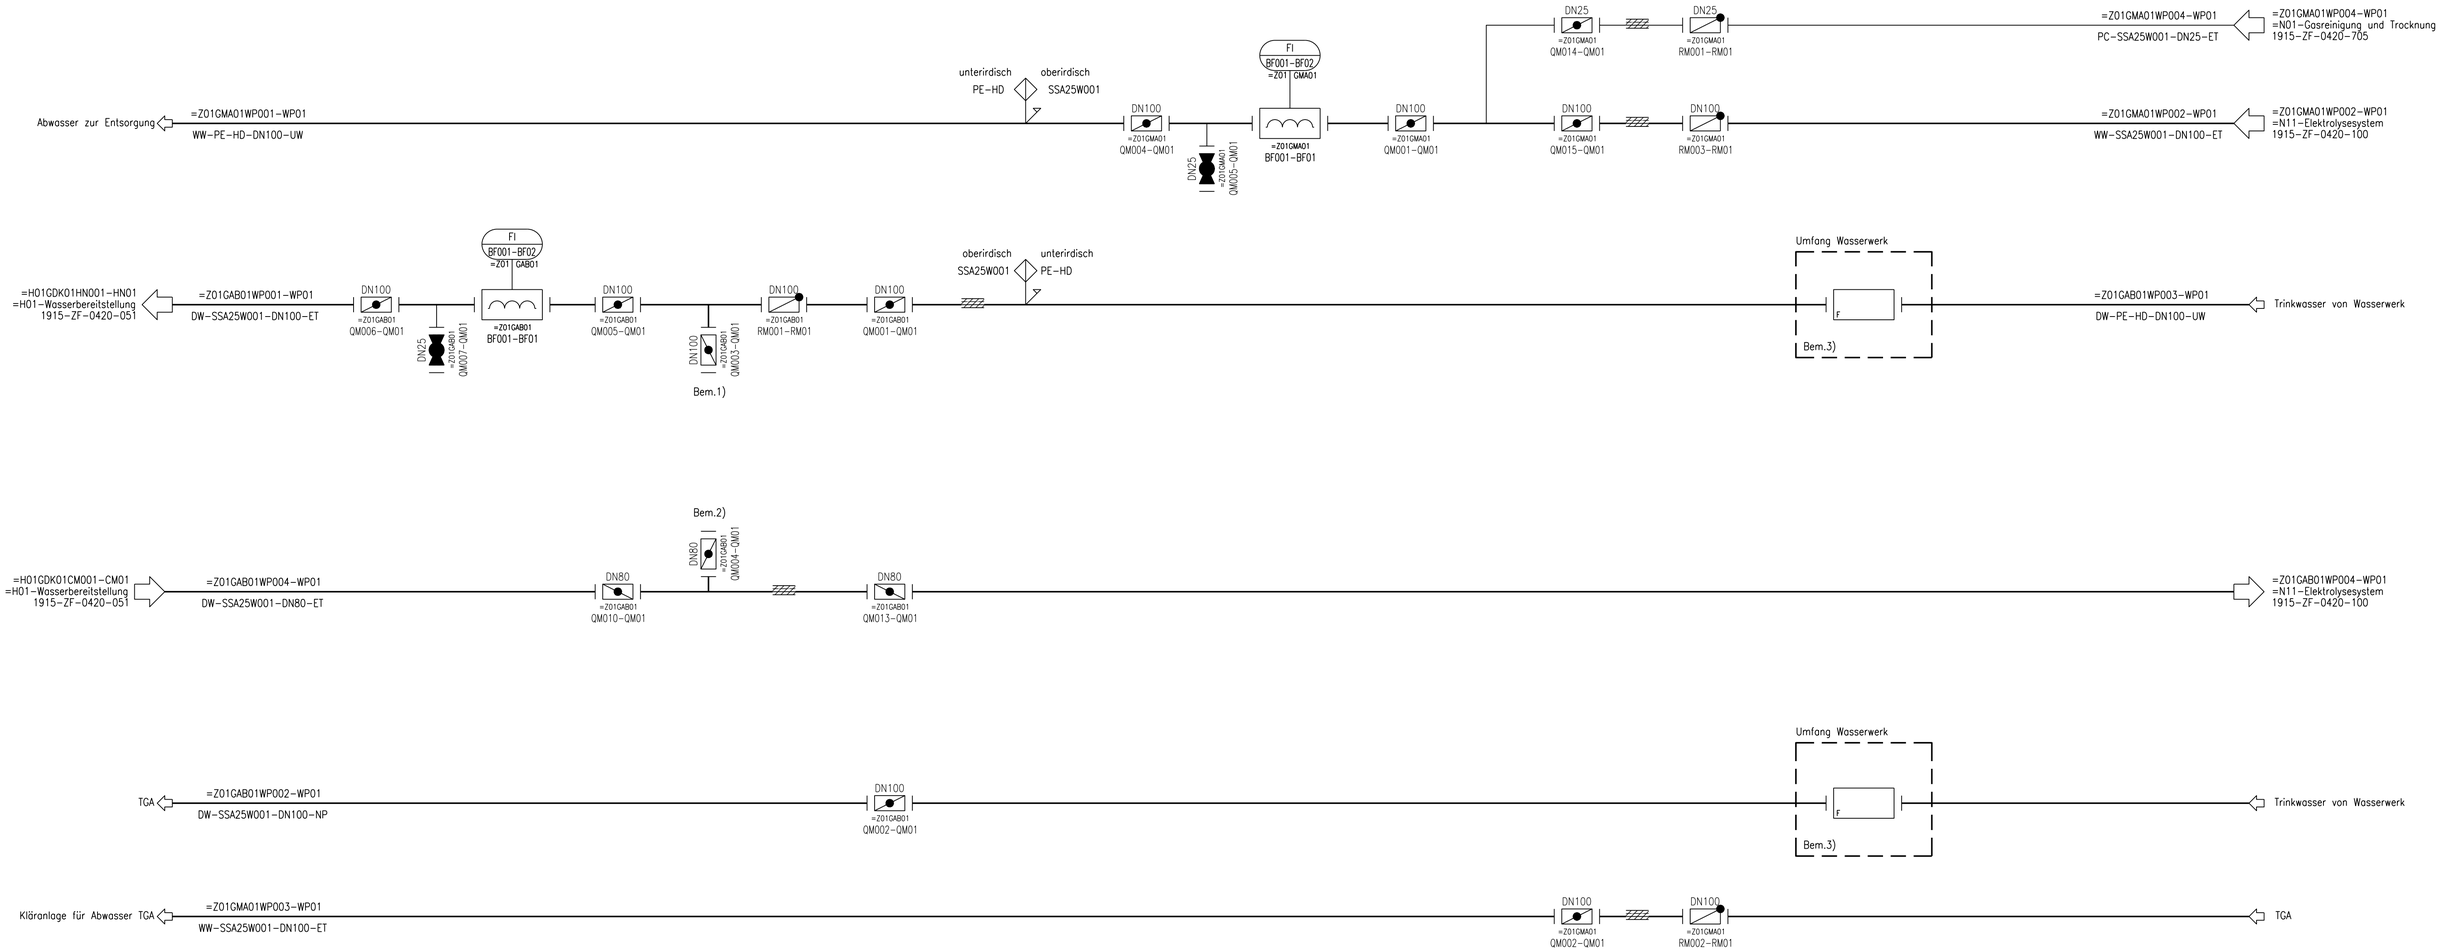


Bemerkungen:

1) Anschluss für Brauchwasser
2) für zukünftige Erweiterung
3) keine Signalaufschaltung auf PLS von CIP

Nr.	Datum	Revision	Zweck der Revision	Bearbeitet	Geprüft	Freigabe Projekt	Freigabe AG
01	04.09.2026		Issued for Approval	JuK	FrT	ToS	
00	24.06.2026		Issued for Approval	JuK	FrT	ToS	

Projekt
Projekt Lotse
Am Bütteler Kanal 1, 25572 Büttel, Deutschland

Bauherr
LOTSE

Benennung
R&I
=Z01-Wassertransport

Owner's Engineer
iPP SKL

verantwortlich
IPP Ingenieurgesellschaft Possel u. Partner GmbH
Rendsburger Landstraße 196-198, 24113 Kiel
Telefon +49 (0)431 684 59-0, Telefax +49 (0)431 684 59-59
www.ipp-gruppe.de

Zeichnungs-Nr. Bauherr

Revision

Zeichnungs-Nr. Ersteller
1915-ZF-0420-055

Revision
01

erstellt
SKL Engineering GmbH
Halberstädter Straße 42, 39112 Magdeburg
Telefon +49 (391) 24 40 55-0, Telefax +49 (391) 24 40 55-10
magdeburg@skl-engineering.de

Gezeichnet	Datum	Geprüft	Datum	Maßstab	Ausgabestufe	Blatt	von	Format
JuK	21.05.2026	EbB	22.05.2026	None	IFA	1	1	A1