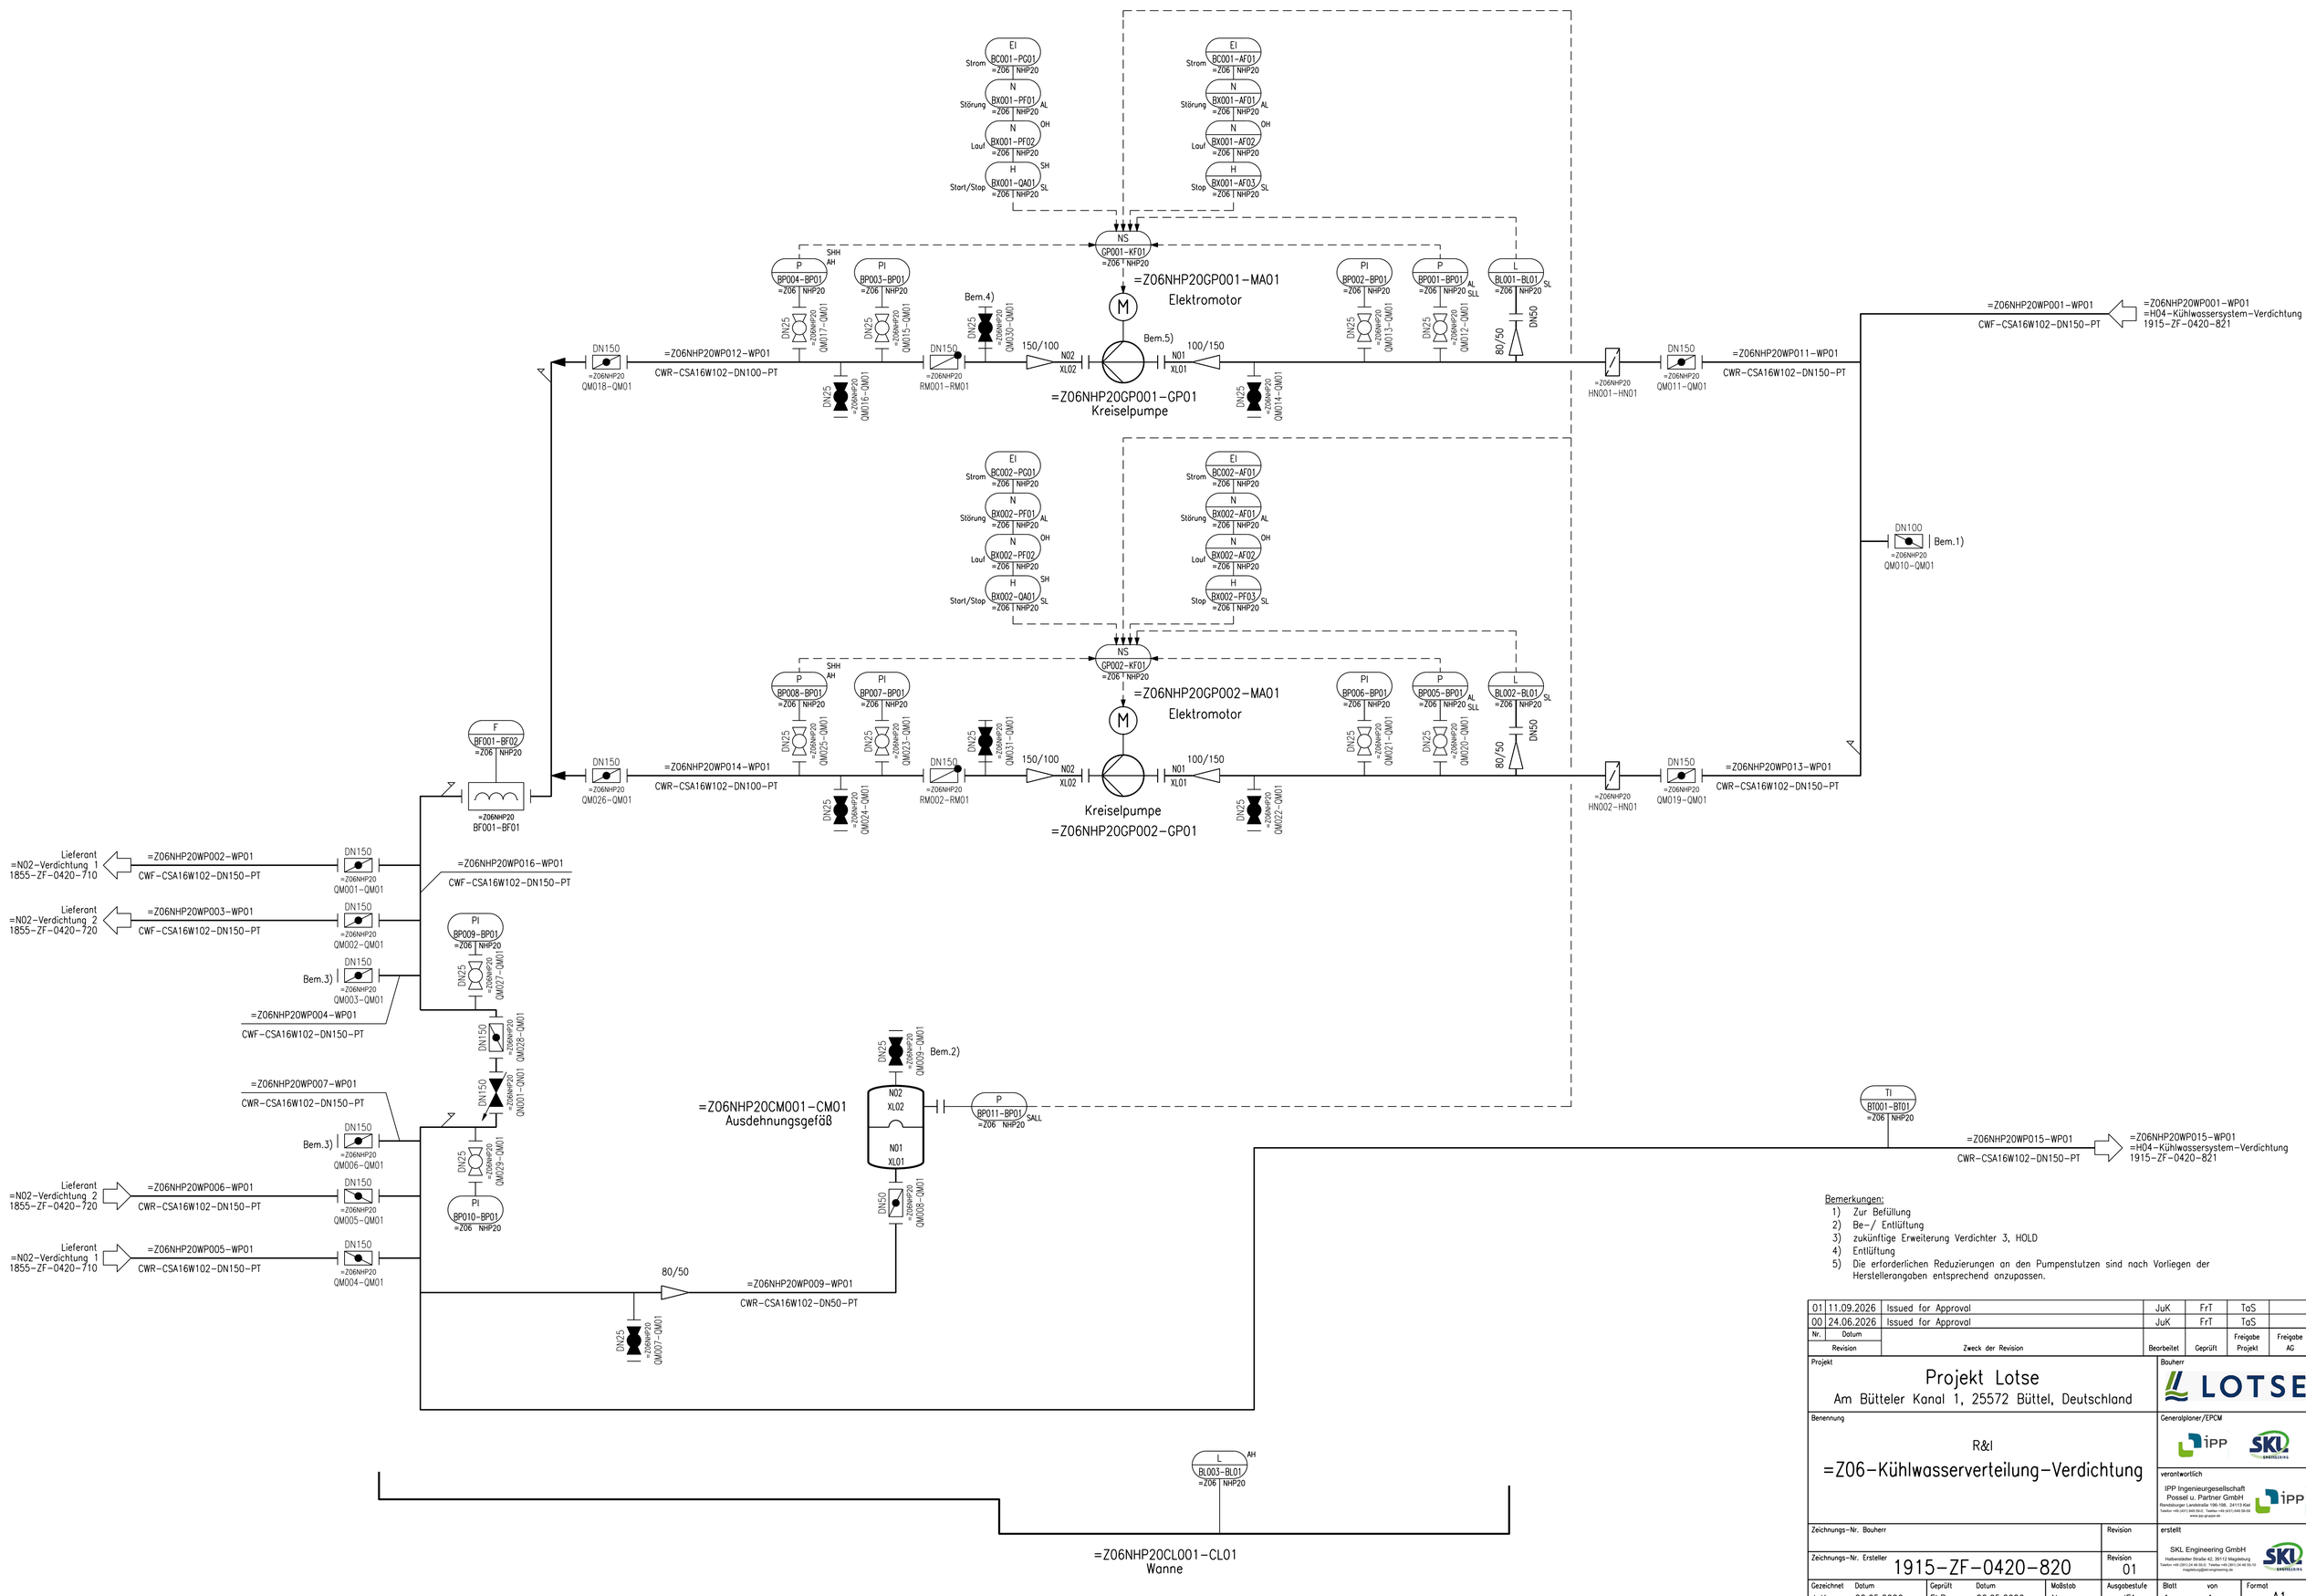


Bemerkungen:

1) Zur Befüllung
2) Be-/ Entlüftung
3) zukünftige Erweiterung Verdichter 3, HOLD
4) Entlüftung
5) Die erforderlichen Reduzierungen an den Pumpenstutzen sind nach Vorliegen der Herstellerangaben entsprechend anzupassen.

Nr.	Datum	Zweck der Revision	Bearbeitet	Geprüft	Freigabe Projekt	Freigabe AG
01	11.09.2026	Issued for Approval	JuK	FrT	ToS	
00	24.06.2026	Issued for Approval	JuK	FrT	ToS	

Projekt
Projekt Lotse
Am Bütteler Kanal 1, 25572 Büttel, Deutschland

Bauherr
LOTSE

Benennung
R&I
=Z06-Kühlwasserverteilung-Verdichtung

Generalplaner/EPCM
iPP SKL ENGINEERING

verantwortlich
IPP Ingenieurgesellschaft Possel u. Partner GmbH
Rendsburger Landstraße 196-198, 24113 Kiel
Telefon +49 (431) 684 59-0, Telefax +49 (431) 684 59-44
www.ipp-ingpos.de

Zeichnungs-Nr. Bauherr
Revision

Zeichnungs-Nr. Ersteller
1915-ZF-0420-820
Revision
01

erstellt
SKL Engineering GmbH
Halberstädter Straße 42, 39112 Magdeburg
Telefon +49 (391) 24 46 55-0, Telefax +49 (391) 24 46 55-10
magdeburg@skl-engineering.de

Gezeichnet	Datum	Geprüft	Datum	Maßstab	Ausgabestufe	Blatt	von	Format
JuK	22.05.2026	EbB	26.05.2026	None	IFA	1	1	A1