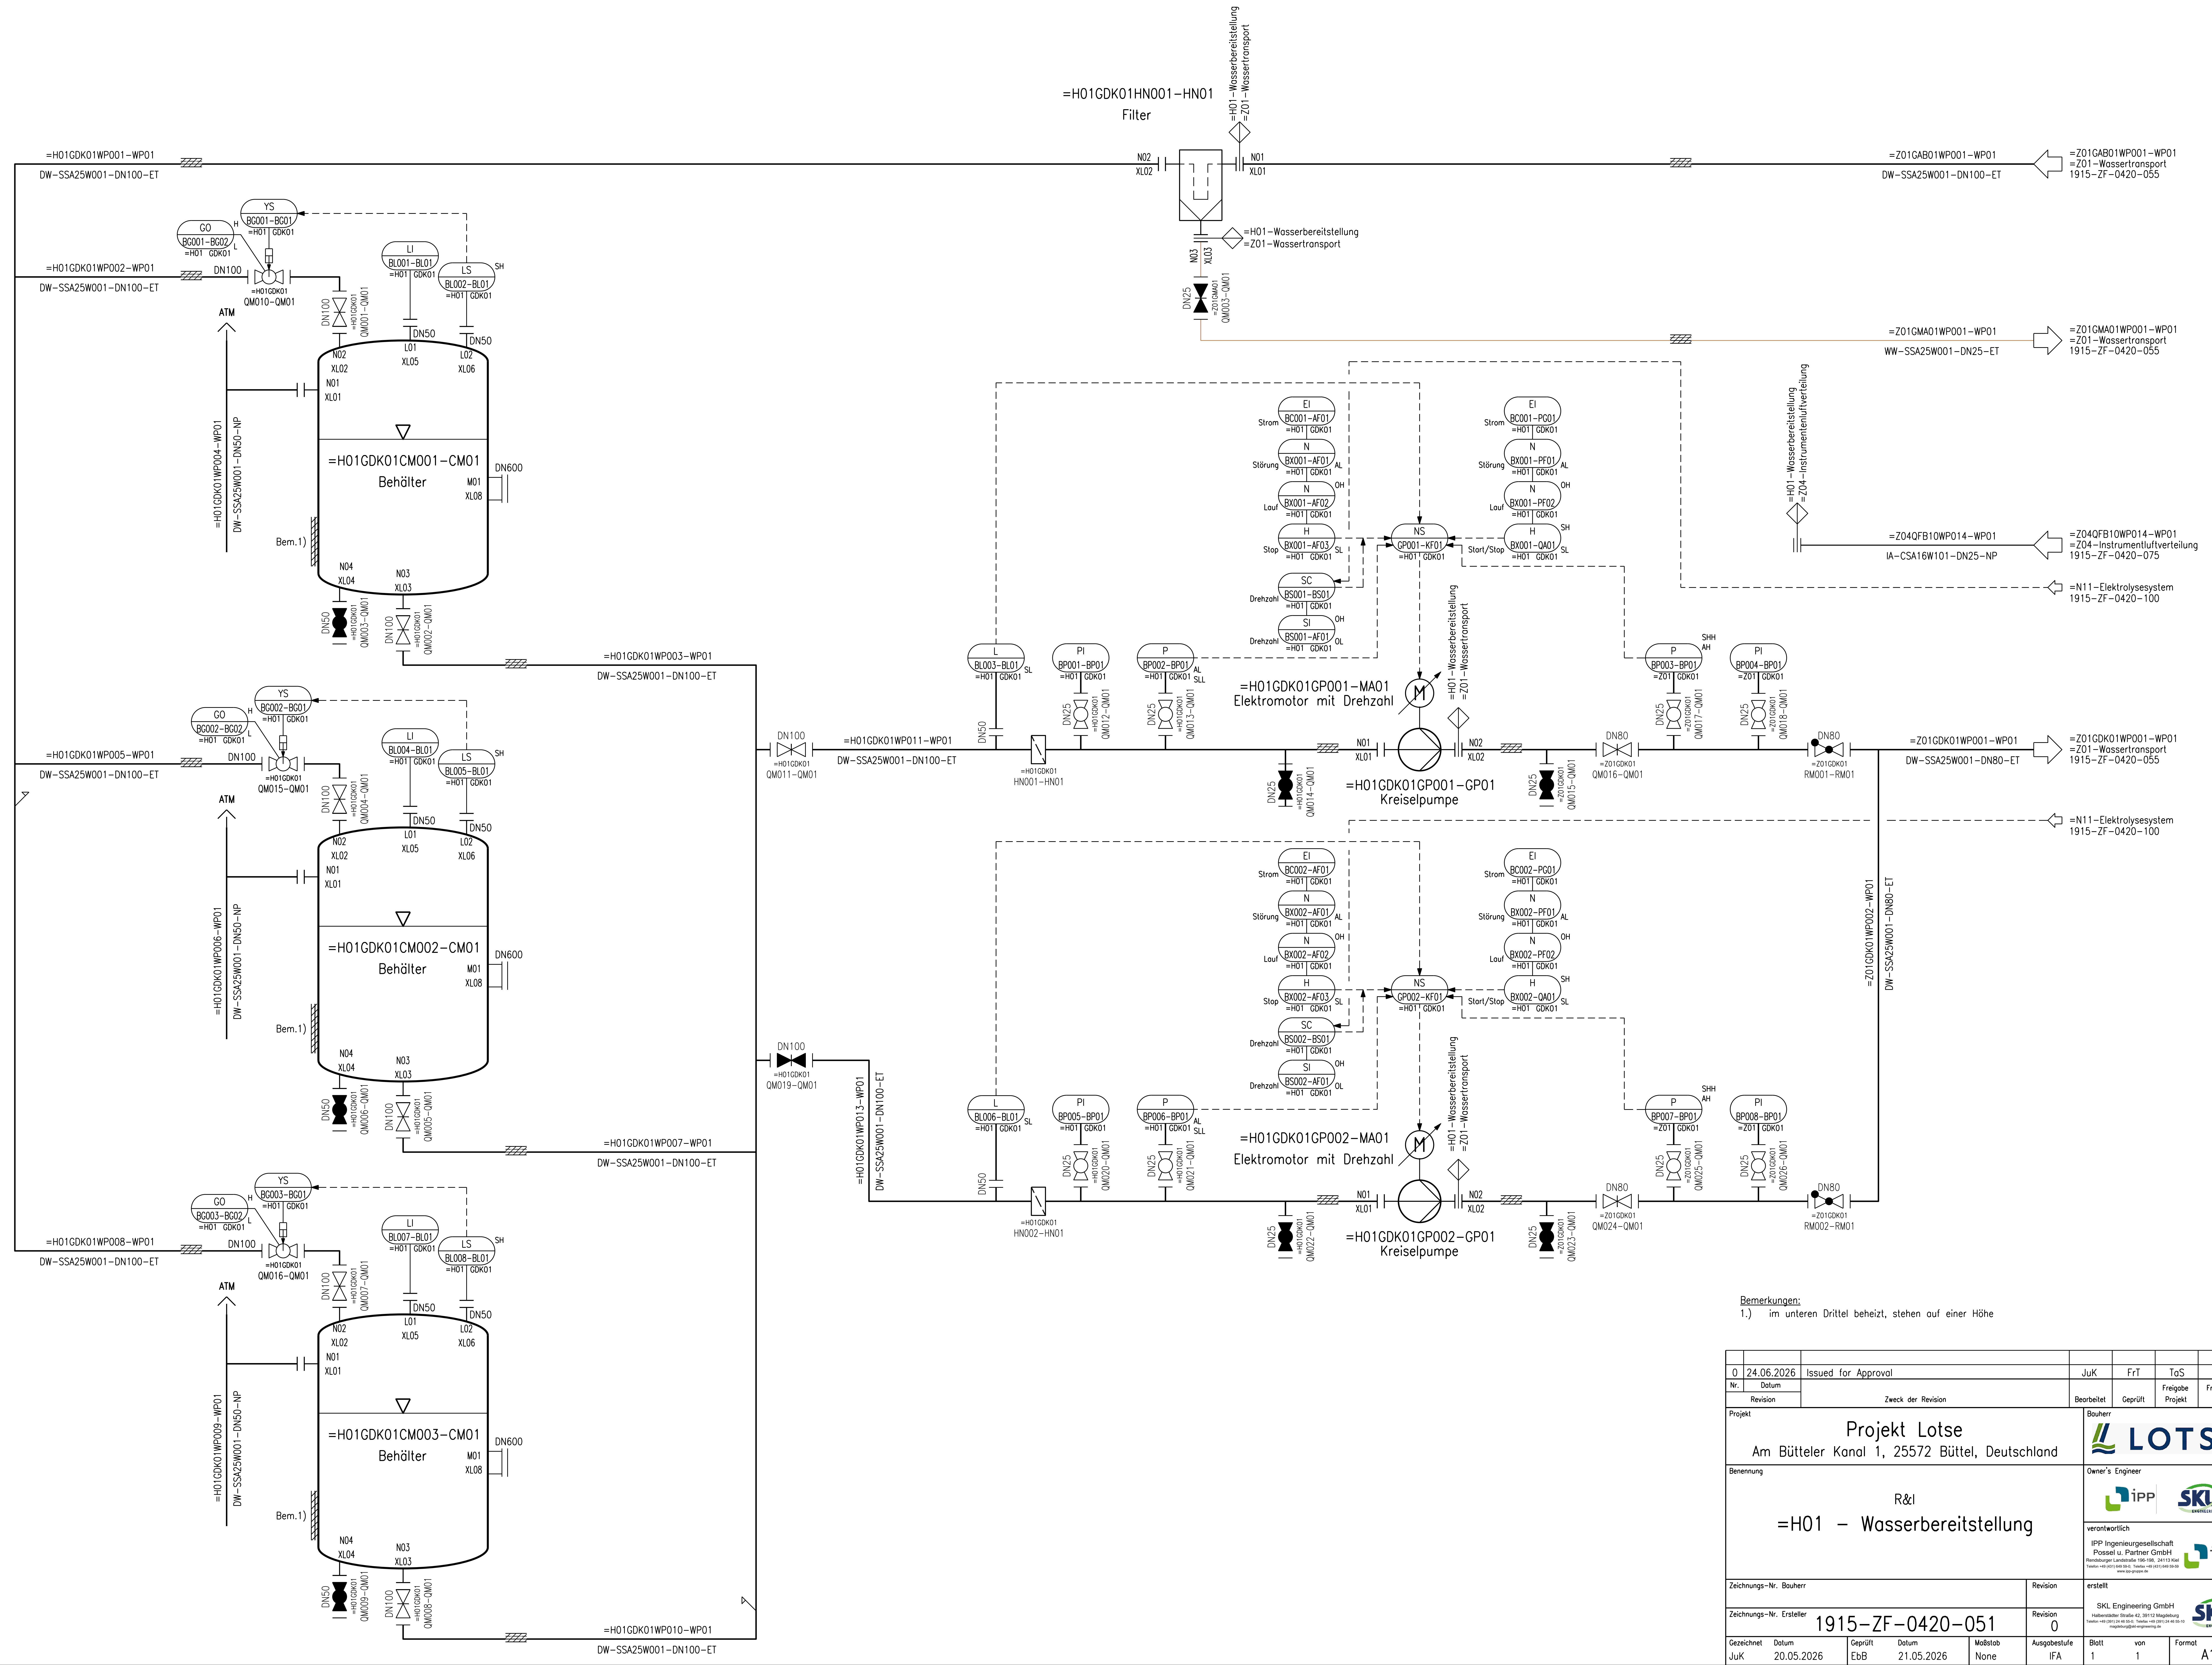
=H01GDK01HN001-HN01
Filter
=H01-Wasserbereitstellung
=Z01-Wassertransport
N02
XL02
N01
XL01
N03
XL03
DN25
QM003-QM01
=H01GDK01WP001-WP01
DW-SSA25W001-DN100-ET
=Z01GAB01WP001-WP01
DW-SSA25W001-DN100-ET
=Z01GAB01WP001-WP01
=Z01-Wassertransport
1915-ZF-0420-055
=Z01GMA01WP001-WP01
WW-SSA25W001-DN25-ET
=Z01GMA01WP001-WP01
=Z01-Wassertransport
1915-ZF-0420-055
=H01GDK01WP002-WP01
DW-SSA25W001-DN100-ET
=H01GDK01WP005-WP01
DW-SSA25W001-DN100-ET
=H01GDK01WP008-WP01
DW-SSA25W001-DN100-ET
GO
BG001-BG02
YS
BG001-BG01
=H01 GDK01
DN100
QM010-QM01
QM001-QM01
LI
BL001-BL01
LS
BL002-BL01
SH
ATM
=H01GDK01WP004-WP01
DW-SSA25W001-DN50-NP
N02
XL02
N01
XL01
L01
XL05
L02
XL06
DN50
=H01GDK01CM001-CM01
Behälter
DN600
M01
XL08
Bem.1)
N04
XL04
N03
XL03
QM003-QM01
QM002-QM01
=H01GDK01WP003-WP01
DW-SSA25W001-DN100-ET
GO
BG002-BG02
YS
BG002-BG01
QM015-QM01
QM004-QM01
LI
BL004-BL01
LS
BL005-BL01
=H01GDK01WP006-WP01
DW-SSA25W001-DN50-NP
=H01GDK01CM002-CM01
Behälter
QM006-QM01
QM005-QM01
=H01GDK01WP007-WP01
DW-SSA25W001-DN100-ET
GO
BG003-BG02
YS
BG003-BG01
QM016-QM01
QM007-QM01
LI
BL007-BL01
LS
BL008-BL01
=H01GDK01WP009-WP01
DW-SSA25W001-DN50-NP
=H01GDK01CM003-CM01
Behälter
QM009-QM01
QM008-QM01
=H01GDK01WP010-WP01
DW-SSA25W001-DN100-ET
DN100
QM011-QM01
=H01GDK01WP011-WP01
DW-SSA25W001-DN100-ET
DN100
QM019-QM01
=H01GDK01WP013-WP01
DW-SSA25W001-DN100-ET
L
BL003-BL01
SL
PI
BP001-BP01
P
BP002-BP01
AL
SLL
QM012-QM01
QM013-QM01
HN001-HN01
EI
BC001-AF01
Strom
N
BX001-AF01
Störung
AL
N
BX001-AF02
Lauf
OH
H
BX001-AF03
Stop
SC
BS001-BS01
Drehzahl
SI
BS001-AF01
Drehzahl
OH
OL
NS
GP001-KF01
EI
BC001-PG01
Strom
N
BX001-PF01
Störung
N
BX001-PF02
Lauf
H
BX001-QA01
Start/Stop
=H01GDK01GP001-MA01
Elektromotor mit Drehzahl
M
=H01GDK01GP001-GP01
Kreiselpumpe
N01
XL01
N02
XL02
QM014-QM01
QM015-QM01
DN80
QM016-QM01
P
BP003-BP01
SHH
AH
=Z01 GDK01
PI
BP004-BP01
QM017-QM01
QM018-QM01
DN80
RM001-RM01
=Z01GDK01WP001-WP01
DW-SSA25W001-DN80-ET
=Z01GDK01WP001-WP01
=Z01-Wassertransport
1915-ZF-0420-055
=N11-Elektrolysesystem
1915-ZF-0420-100
=H01-Wasserbereitstellung
=Z04-Instrumentenluftverteilung
=Z04QFB10WP014-WP01
IA-CSA16W101-DN25-NP
=Z04QFB10WP014-WP01
=Z04-Instrumentluftverteilung
1915-ZF-0420-075
=N11-Elektrolysesystem
1915-ZF-0420-100
=Z01GDK01WP002-WP01
DW-SSA25W001-DN80-ET
L
BL006-BL01
PI
BP005-BP01
P
BP006-BP01
QM020-QM01
QM021-QM01
HN002-HN01
EI
BC002-AF01
N
BX002-AF01
N
BX002-AF02
H
BX002-AF03
SC
BS002-BS01
SI
BS002-AF01
NS
GP002-KF01
EI
BC002-PG01
N
BX002-PF01
N
BX002-PF02
H
BX002-QA01
=H01GDK01GP002-MA01
Elektromotor mit Drehzahl
=H01GDK01GP002-GP01
Kreiselpumpe
QM022-QM01
QM023-QM01
DN80
QM024-QM01
P
BP007-BP01
PI
BP008-BP01
QM025-QM01
QM026-QM01
DN80
RM002-RM01

Bemerkungen:
1.) im unteren Drittel beheizt, stehen auf einer Höhe

0	24.06.2026	Issued for Approval	JuK	FrT	TaS	
Nr.	Datum					
Revision		Zweck der Revision	Bearbeitet	Geprüft	Freigabe Projekt	Freigabe AG

Projekt

Projekt Lotse
Am Bütteler Kanal 1, 25572 Büttel, Deutschland

Bauherr

Benennung

R&I
=H01 – Wasserbereitstellung

Owner's Engineer

verantwortlich
IPP Ingenieurgesellschaft
Possel u. Partner GmbH
Rendsburger Landstraße 196-198, 24113 Kiel
Telefon +49 (431) 649 59-0; Telefax +49 (431) 649 59-59
www.ipp-gruppe.de

Zeichnungs-Nr. Bauherr
Revision

Zeichnungs-Nr. Ersteller 1915-ZF-0420-051
Revision 0

erstellt
SKL Engineering GmbH
Halberstädter Straße 42, 39112 Magdeburg
Telefon +49 (391) 24 46 55-0; Telefax +49 (391) 24 46 55-10
magdeburg@skl-engineering.de

Gezeichnet	Datum	Geprüft	Datum	Maßstab	Ausgabestufe	Blatt	von	Format
JuK	20.05.2026	EbB	21.05.2026	None	IFA	1	1	A1