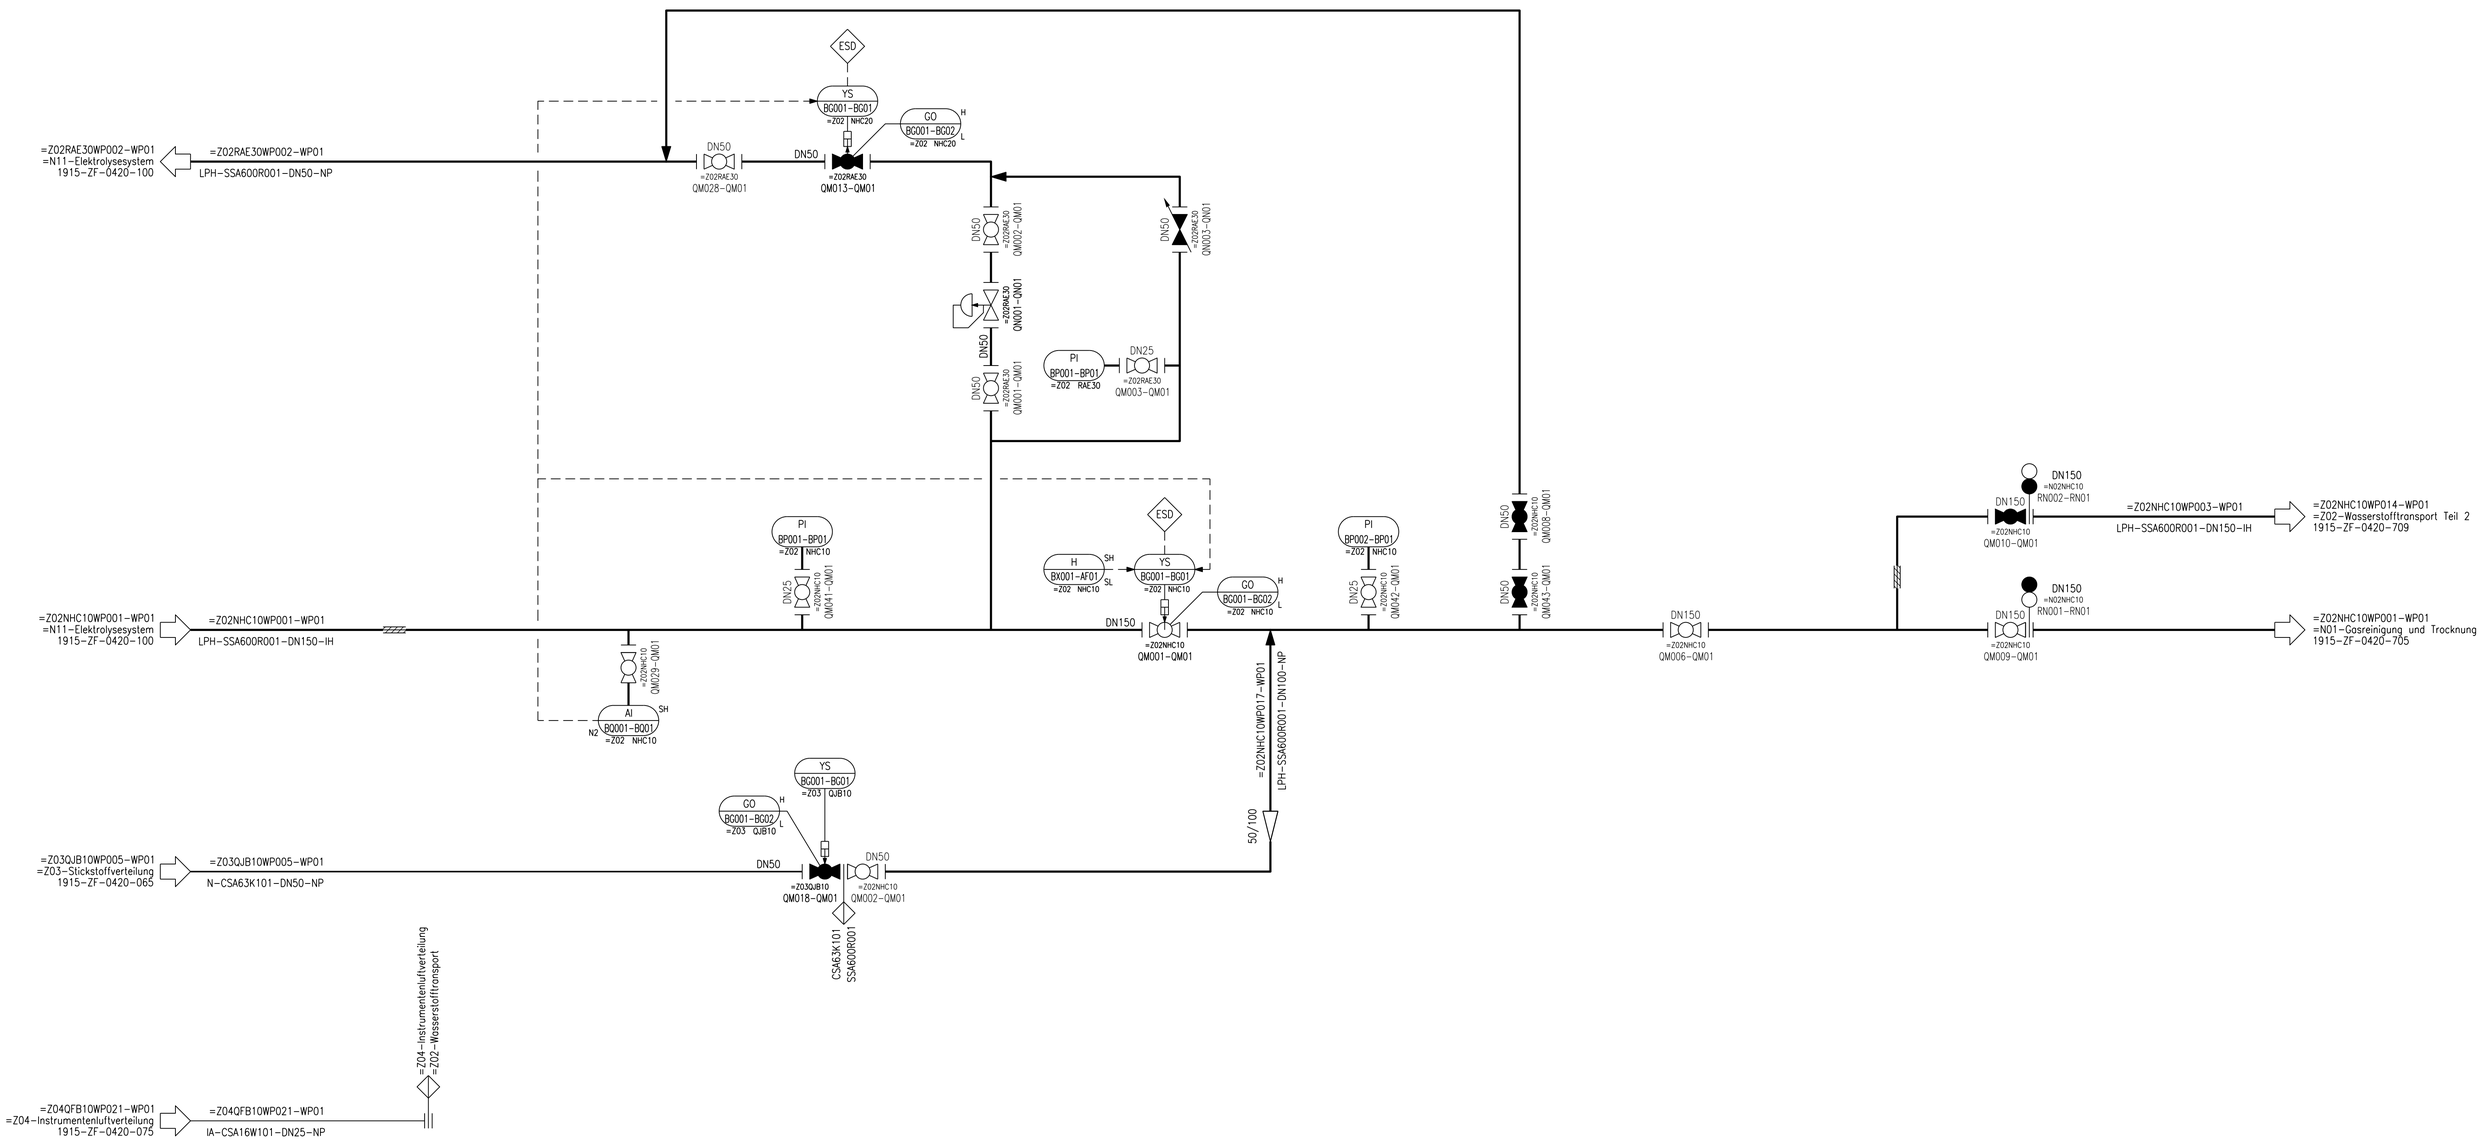


Nr.	Datum	Revision	Zweck der Revision	Bearbeitet	Geprüft	Freigabe Projekt	Freigabe AG
0	24.06.2026		Issued for Approval	JuK	FrT	ToS	

Projekt
Projekt Lotse
Am Bütteler Kanal 1, 25572 Büttel, Deutschland

Bauherr
LOTSE

Benennung
R&I
=Z02-Wasserstofftransport
Teil 1

Owner's Engineer
iPP SKL ENGINEERING

verantwortlich
IPP Ingenieurgesellschaft Possel u. Partner GmbH
Rendsburger Landstraße 106-108, 24113 Kiel
Telefon +49 (431) 684 59-0, Telefax +49 (431) 684 59-44
www.ipp-projekt.de

Zeichnungs-Nr. Bauherr
Revision

Zeichnungs-Nr. Ersteller
1915-ZF-0420-700
Revision 0

erstellt
SKL Engineering GmbH
Halberstädter Straße 42, 39112 Magdeburg
Telefon +49 (391) 24 40 35-0, Telefax +49 (391) 24 40 35-10
magdeburg@skl-engineering.de

Gezeichnet	Datum	Geprüft	Datum	Maßstab	Ausgabestufe	Blatt	von	Format
JuK	21.05.2026	EbB	22.05.2026	None	IFA	1	1	A1